


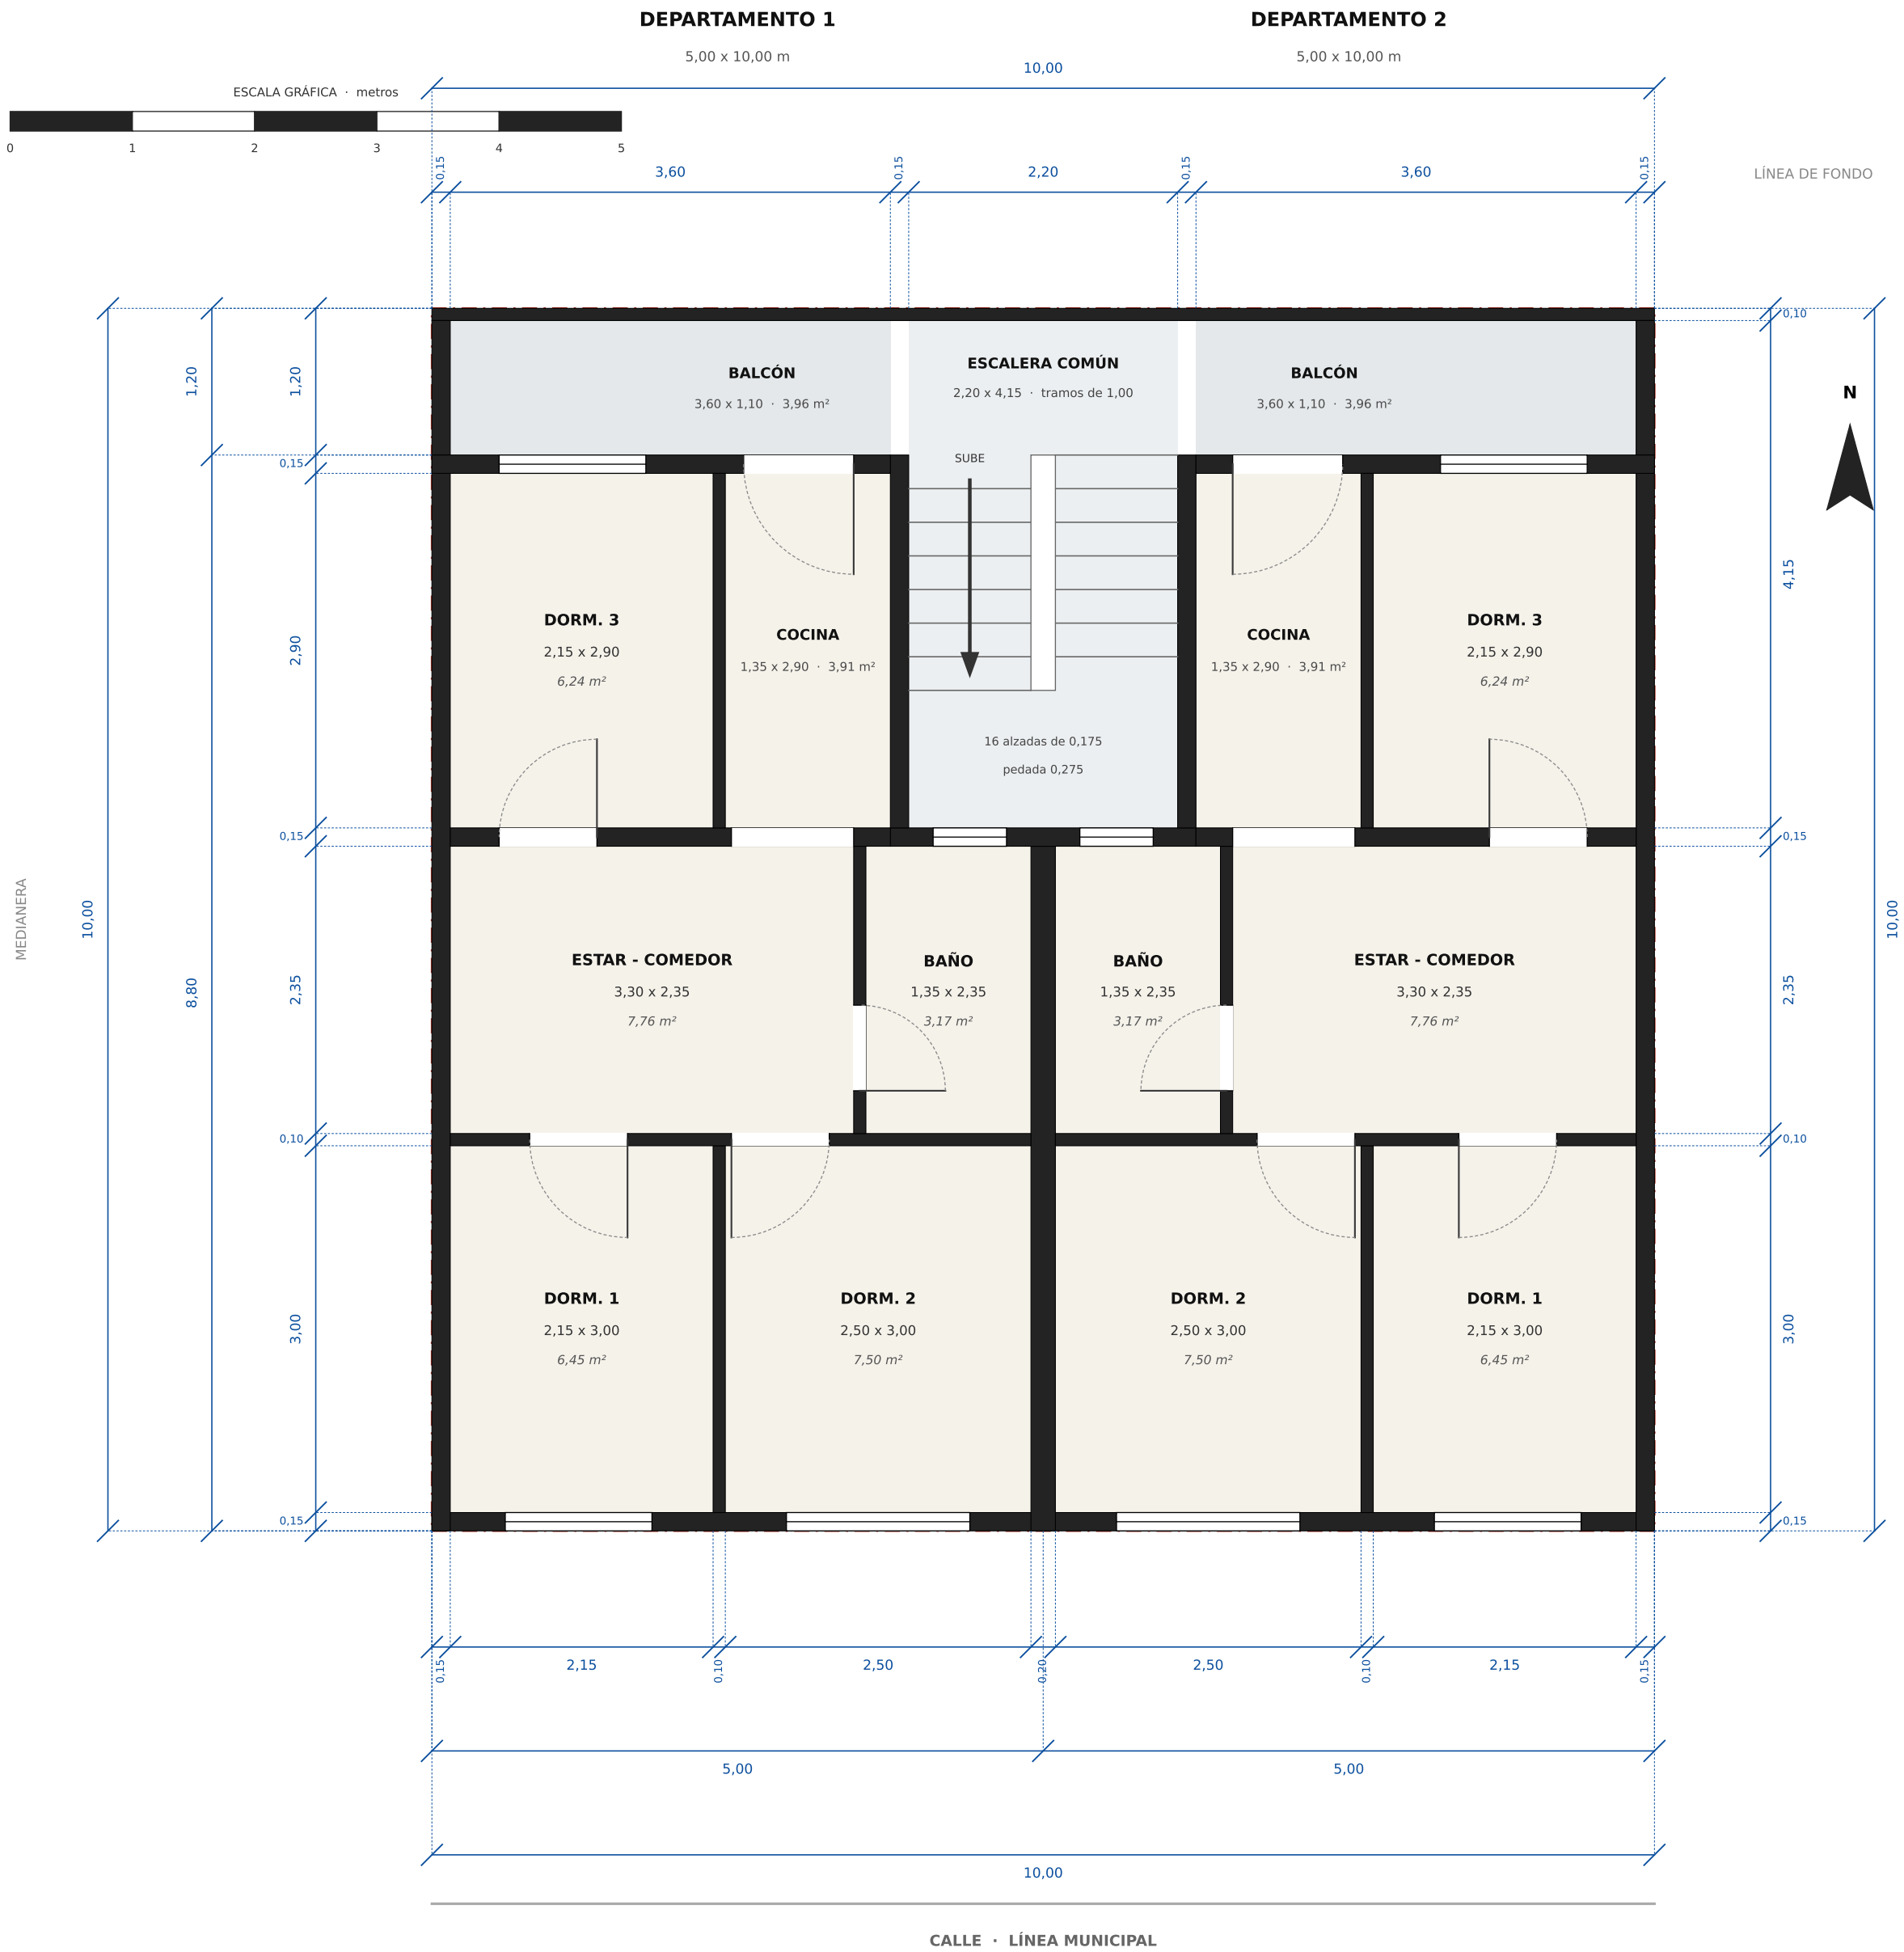

EDIFICIO DE DOS DEPARTAMENTOS		
Terreno de 10,00 x 10,00 m		
PLANTA ACOTADA		
3 dormitorios por unidad · planta baja y alta idénticas		
Escala	1 : 50	
Acotación	metros	
Muros exteriores / medianeras	0,15 m	
Muro divisorio	0,20 m	
Tabiques interiores	0,10 m	
Altura piso a piso	2,80 m	
Balcón corredor (fondo)	1,20 m	
Escalera común	2,20 x 4,15 m	
PLANILLA DE SUPERFICIES		
Por departamento (5,00 x 10,00)		
Dorm. 1	2,15 x 3,00	6,45 m²
Dorm. 2	2,50 x 3,00	7,50 m²
Estar - Comedor	3,30 x 2,35	7,76 m²
Baño	1,35 x 2,35	3,17 m²
Dorm. 3	2,15 x 2,90	6,24 m²
Cocina	1,35 x 2,90	3,91 m²
Balcón	3,60 x 1,10	3,96 m²
Superficie cubierta	35,03 m²	
Total con balcón	38,99 m²	
Edificio completo: 4 departamentos		
(2 por planta, planta baja y alta)		
NOTAS		
1. Medidas en metros, tomadas a cara de muro terminado.		
2. Sin pasillo: el estar-comedor es el distribuidor y todas las puertas abren sobre él. Se abre a la cocina por un vano libre de 1,00 m.		
3. Los dos departamentos son espejo respecto del muro divisorio.		
4. Acceso a la planta alta por escalera común al fondo, de dos tramos con descanso, y balcón corredor de 1,20 m.		
5. Muros laterales sobre medianera: sin aberturas. Los tres dormitorios ventilan a fachada (dos al frente, uno al balcón).		
6. El estar-comedor queda interior: recibe luz a través de la cocina y el balcón.		
7. El baño ventila a la caja de escalera, que funciona como patio de aire y luz.		
8. Verificar retiros, altura y factor de ocupación con la ordenanza municipal.		
9. Cotas a confirmar con relevamiento en obra.		